


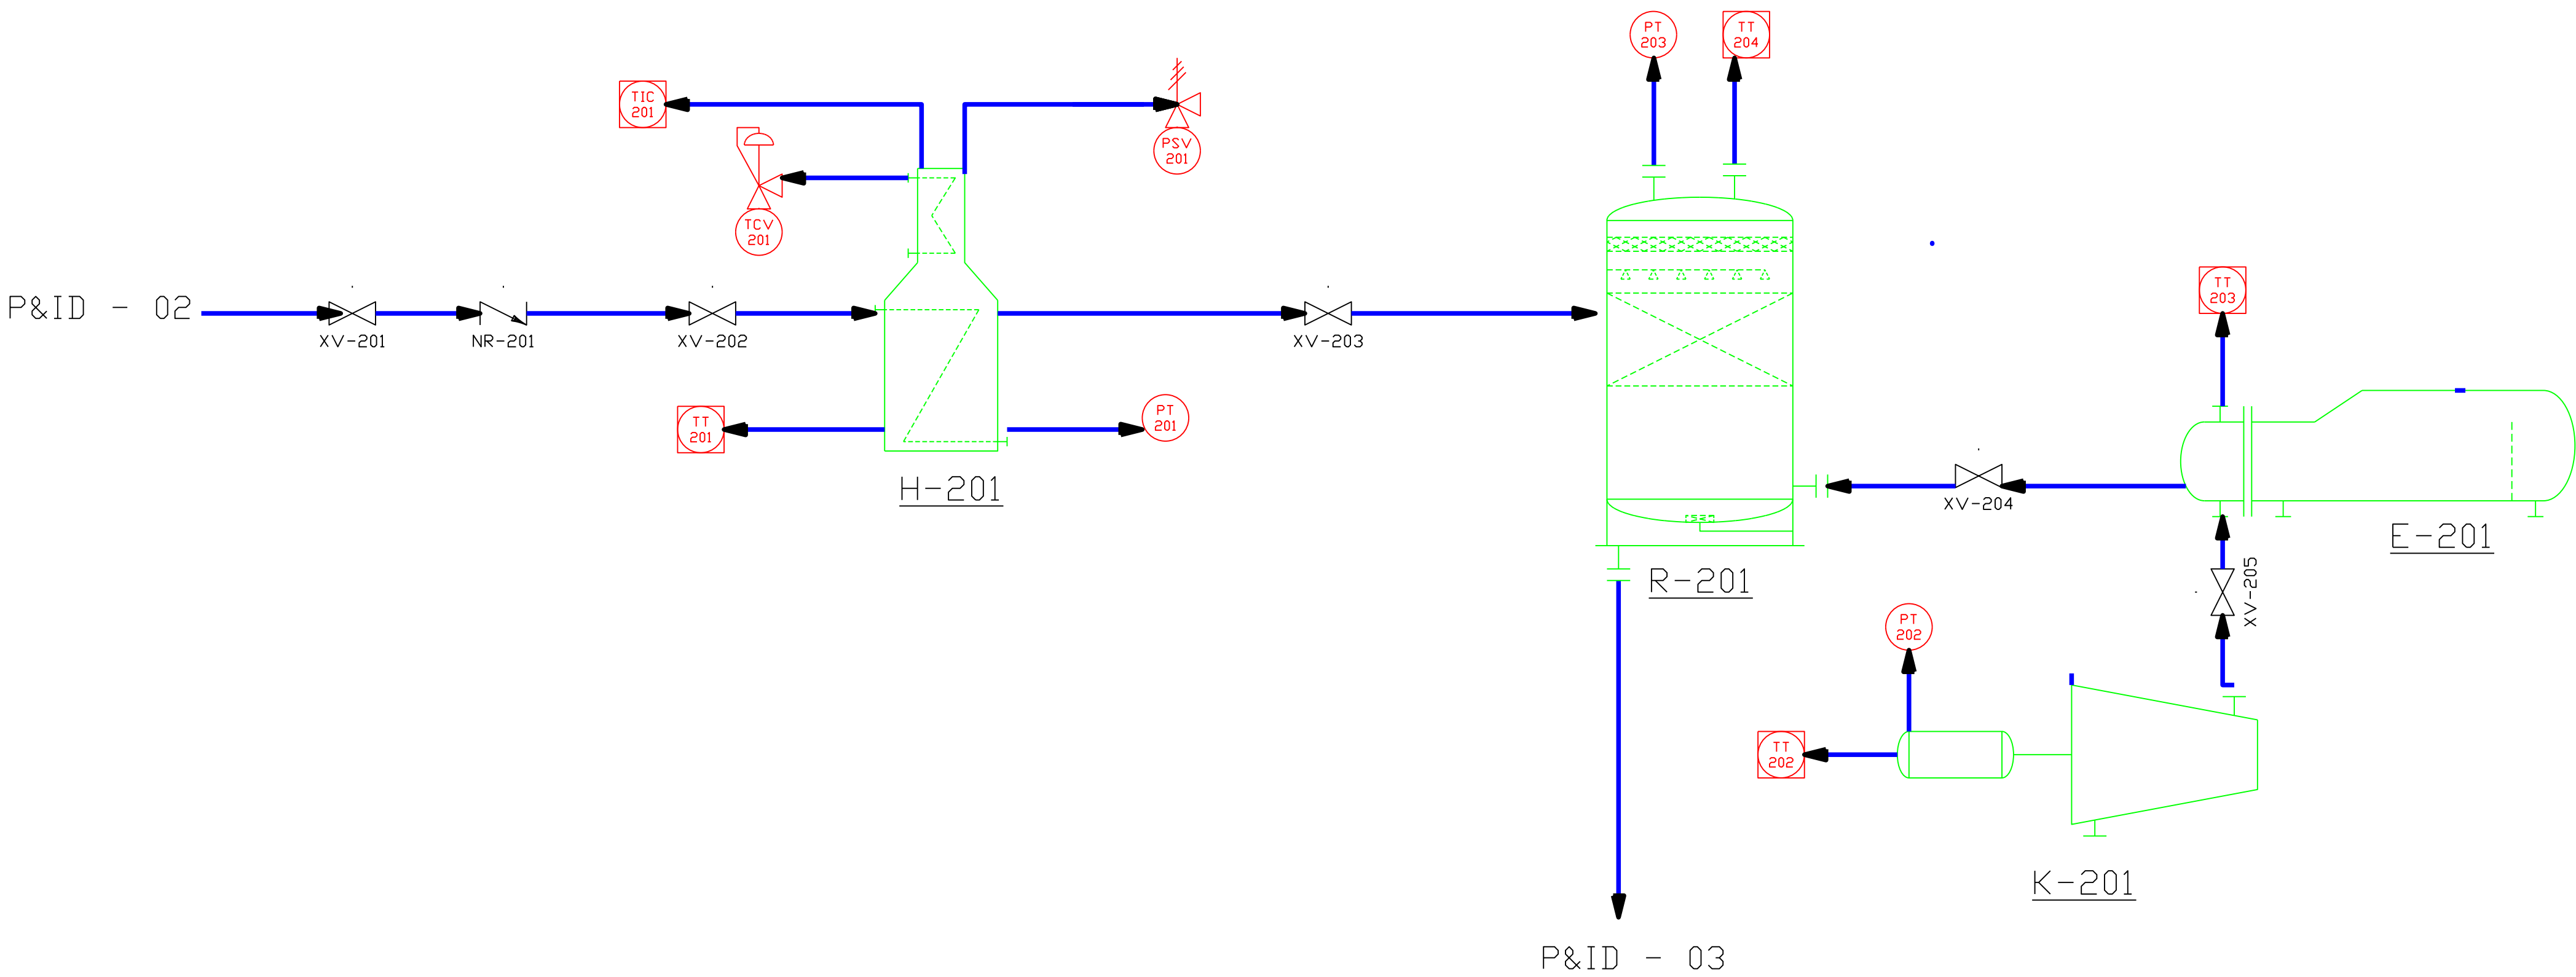

General Notes

No.	Revision/Issue	Date

Drawing Name
Ammonia P&ID 02
####

Project Name and Address
Ammonia_Plant_PID
Greenfield Conventional Ammonia Plant

Area	Stomp
####	
Drawing Number	
####	
Author	
sadiq	