


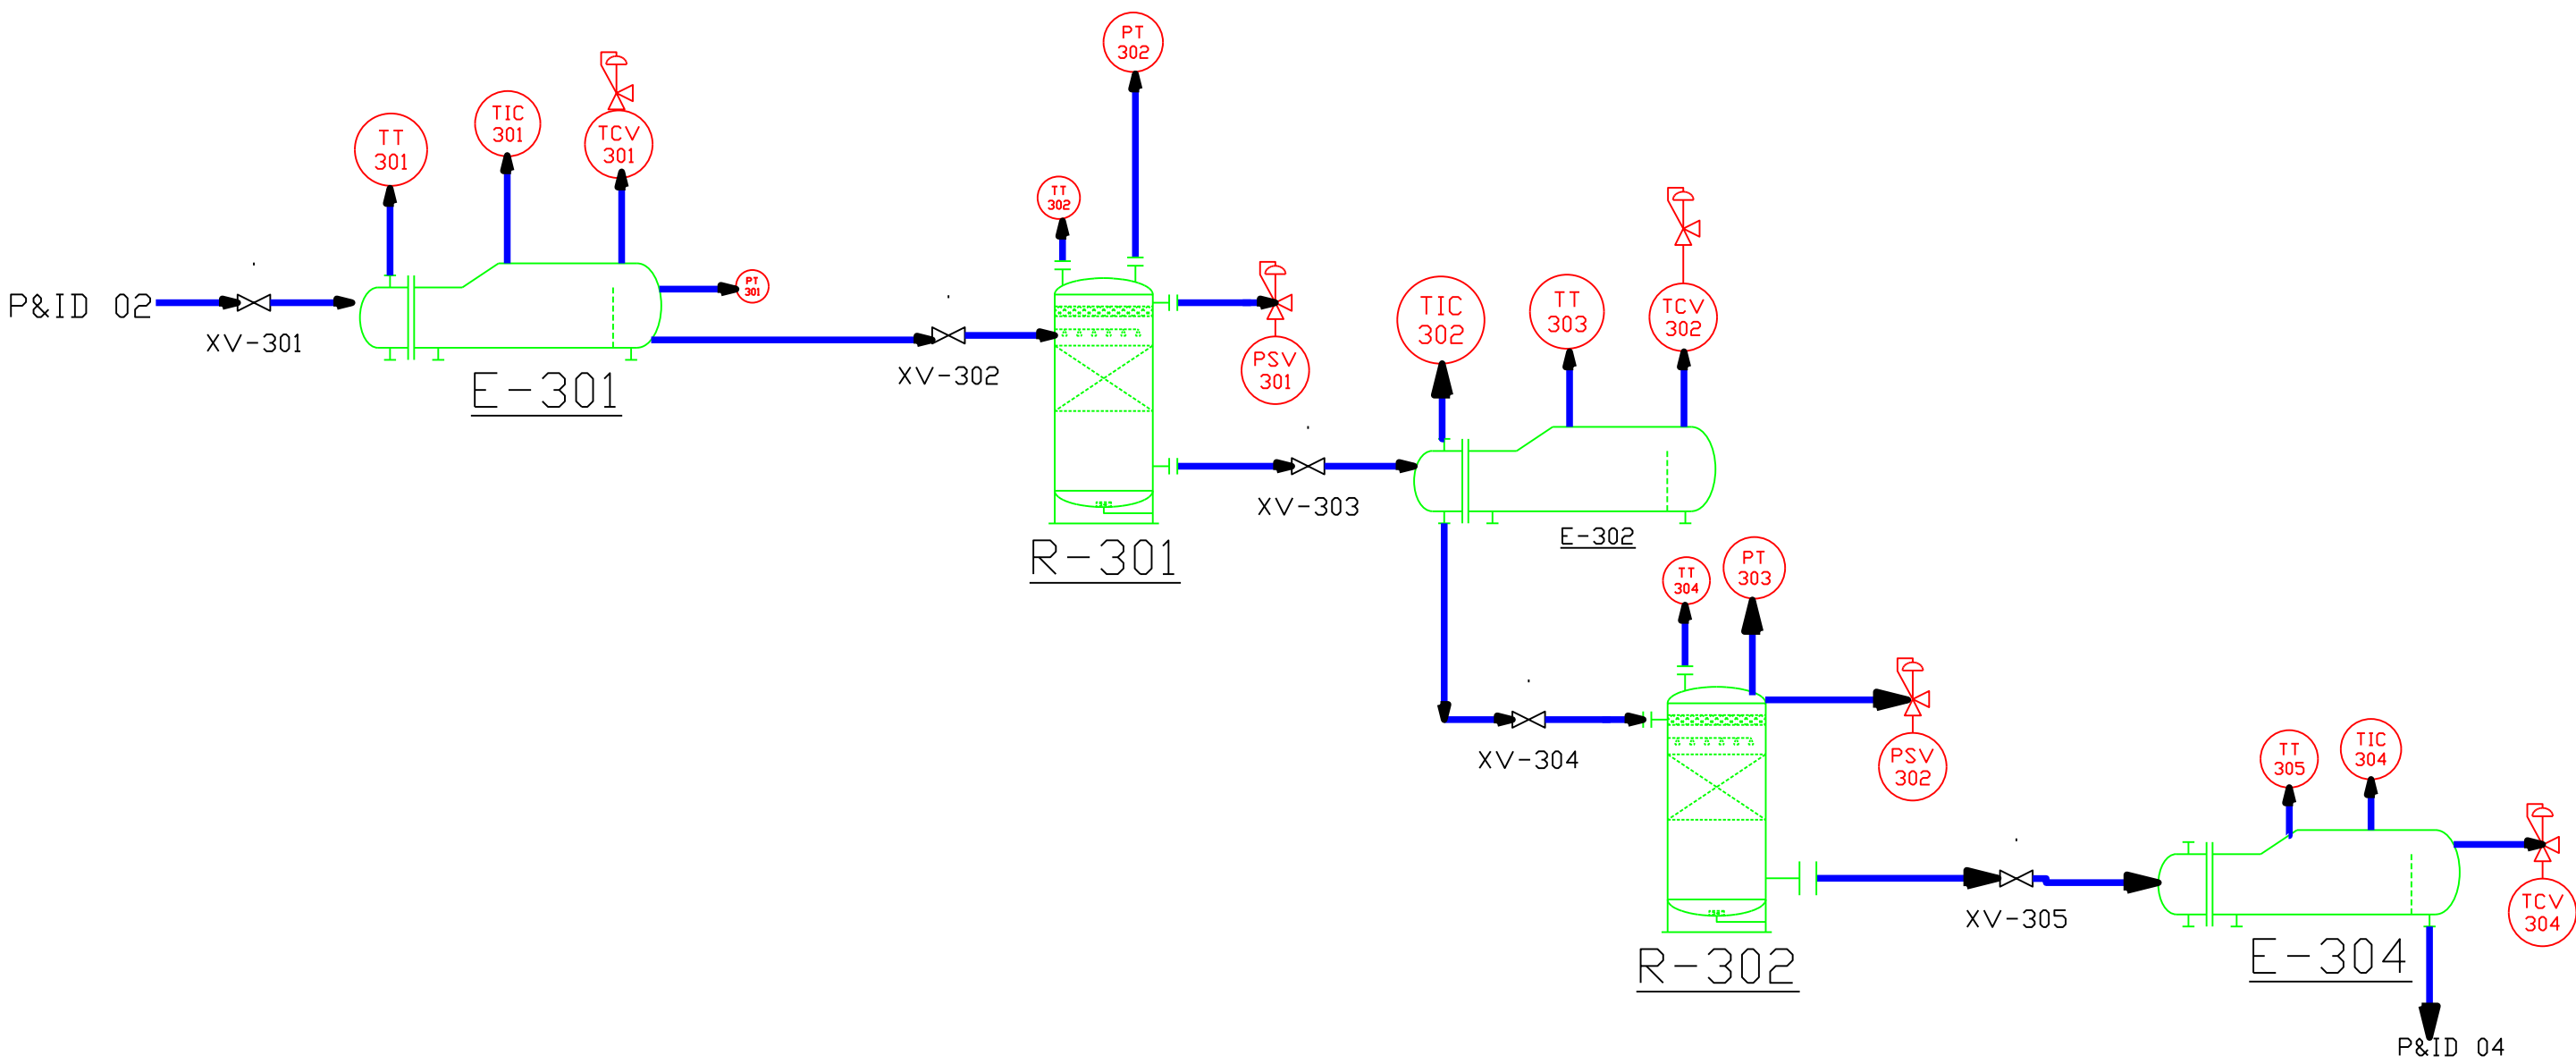

General Notes

No.	Revision/Issue	Date

Drawing Name

Ammonia P&ID 03

####

Project Name and Address

Ammonia_Plant_PID

Greenfield Conventional Ammonia Plant

Area	####	Stomp
Drawing Number	####	
Author	sadiq	