


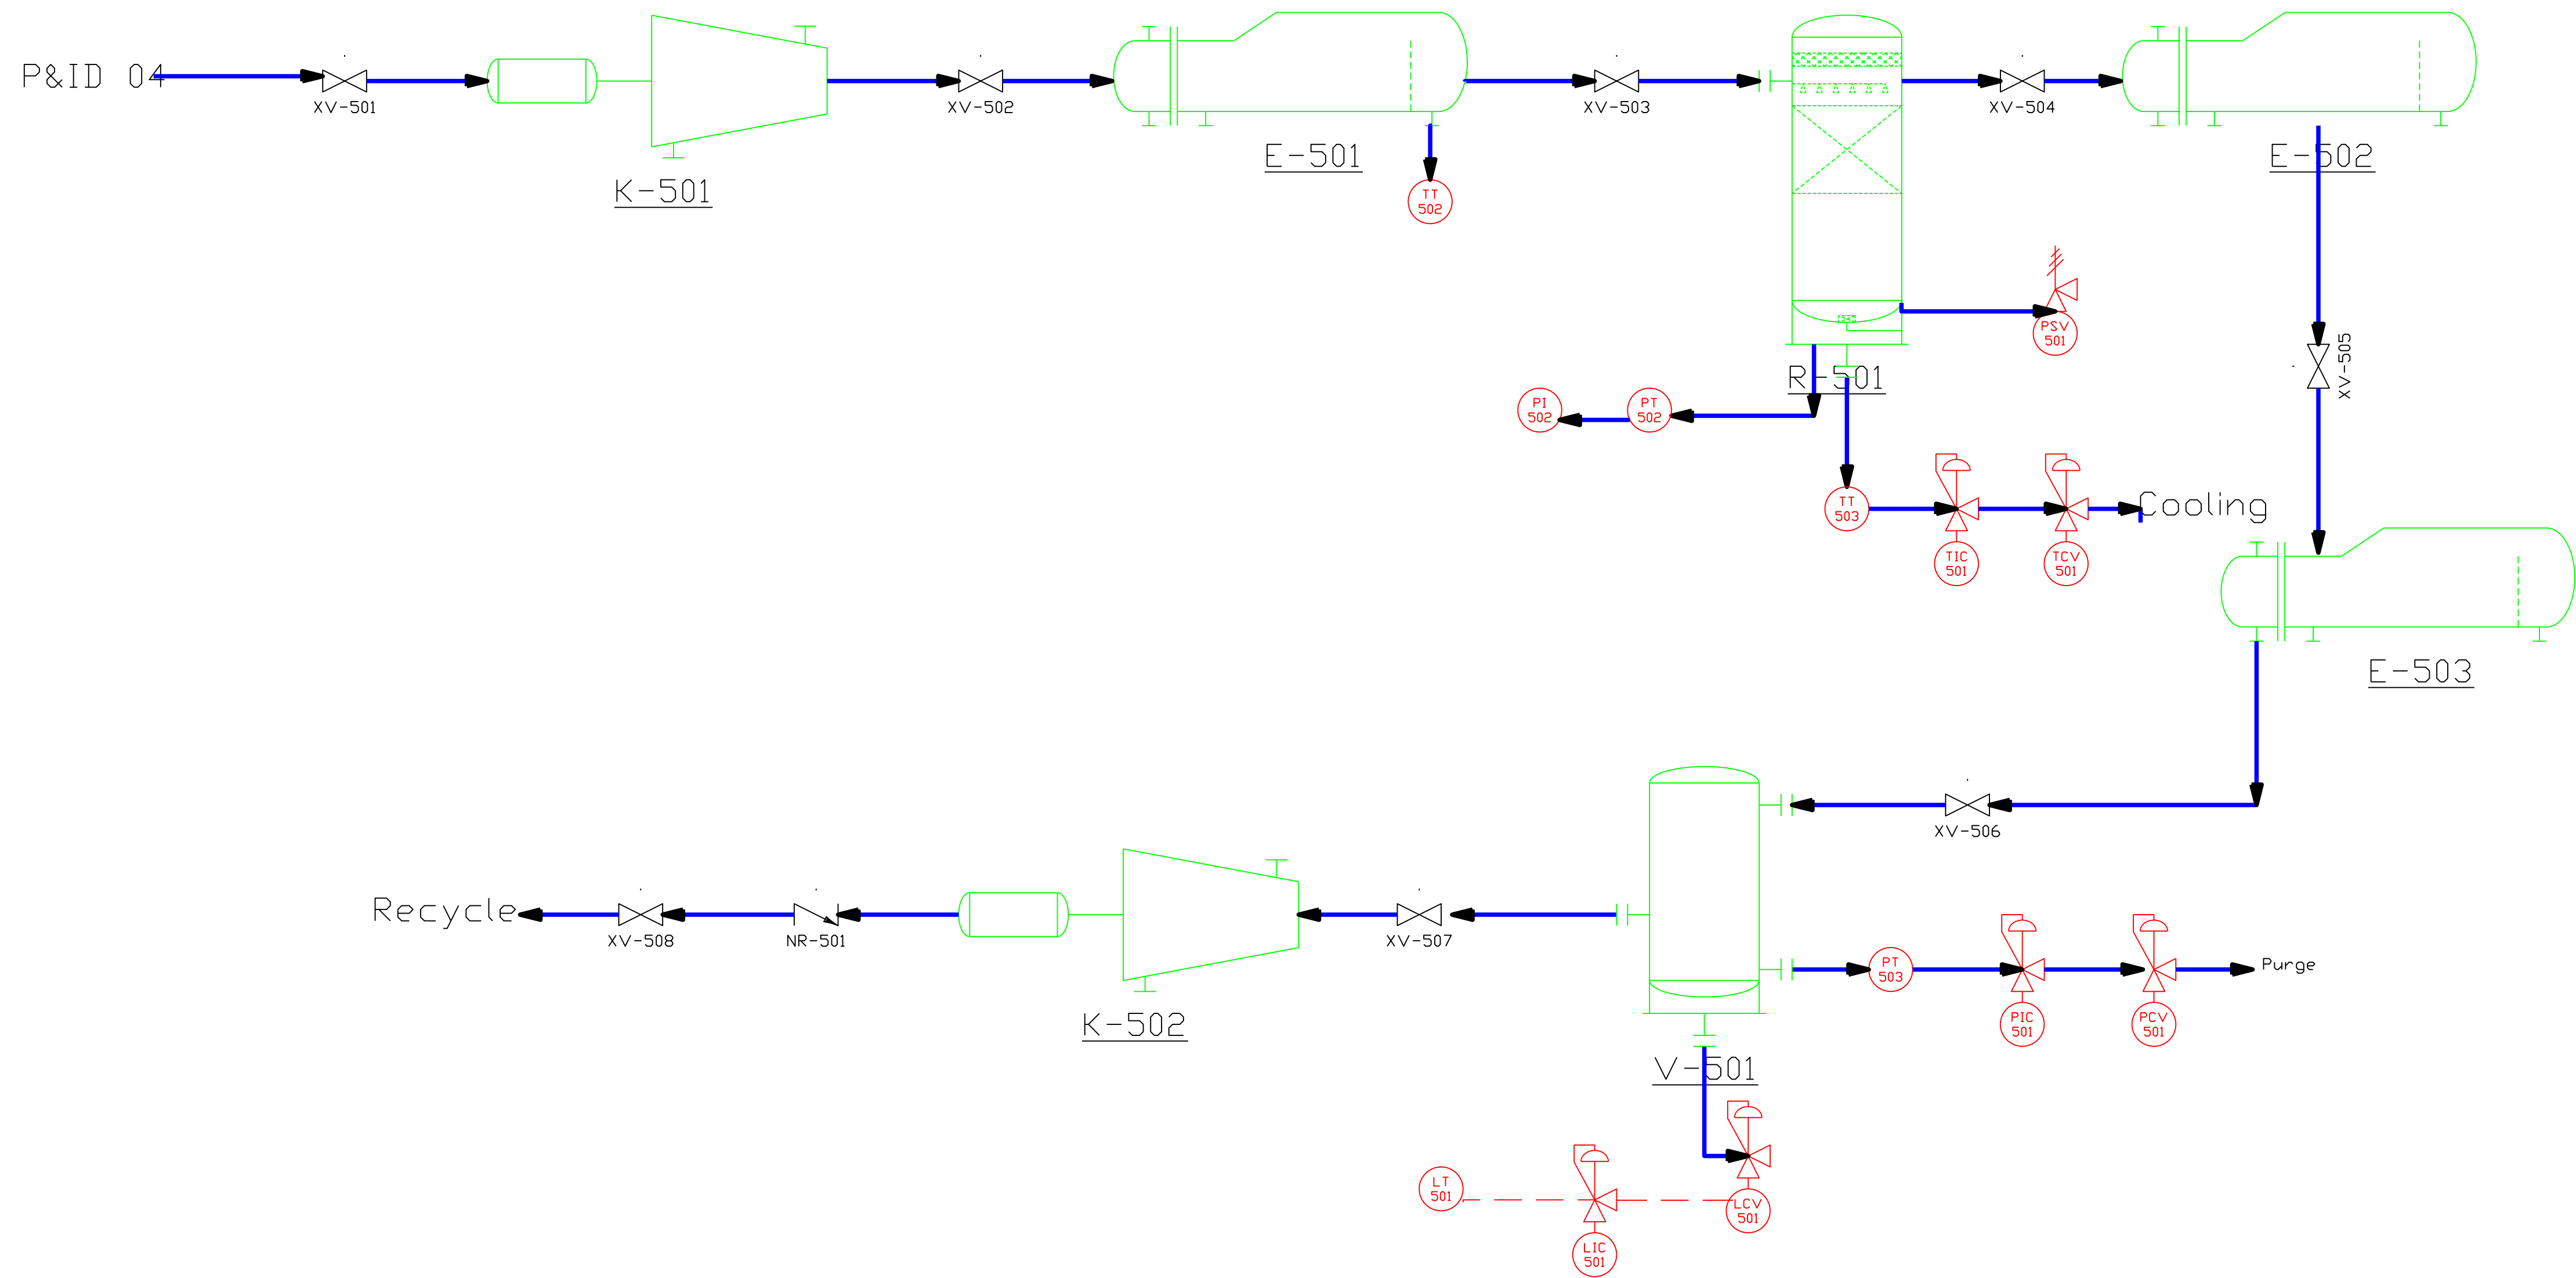

General Notes

No.	Revision/Issue	Date

Drawing Name
Ammonia P&ID 05
####

Project Name and Address
Ammonia_Plant_PID
Greenfield Conventional Ammonia Plant

Area ####	Stomp
Drawing Number ####	
Author sadiq	